


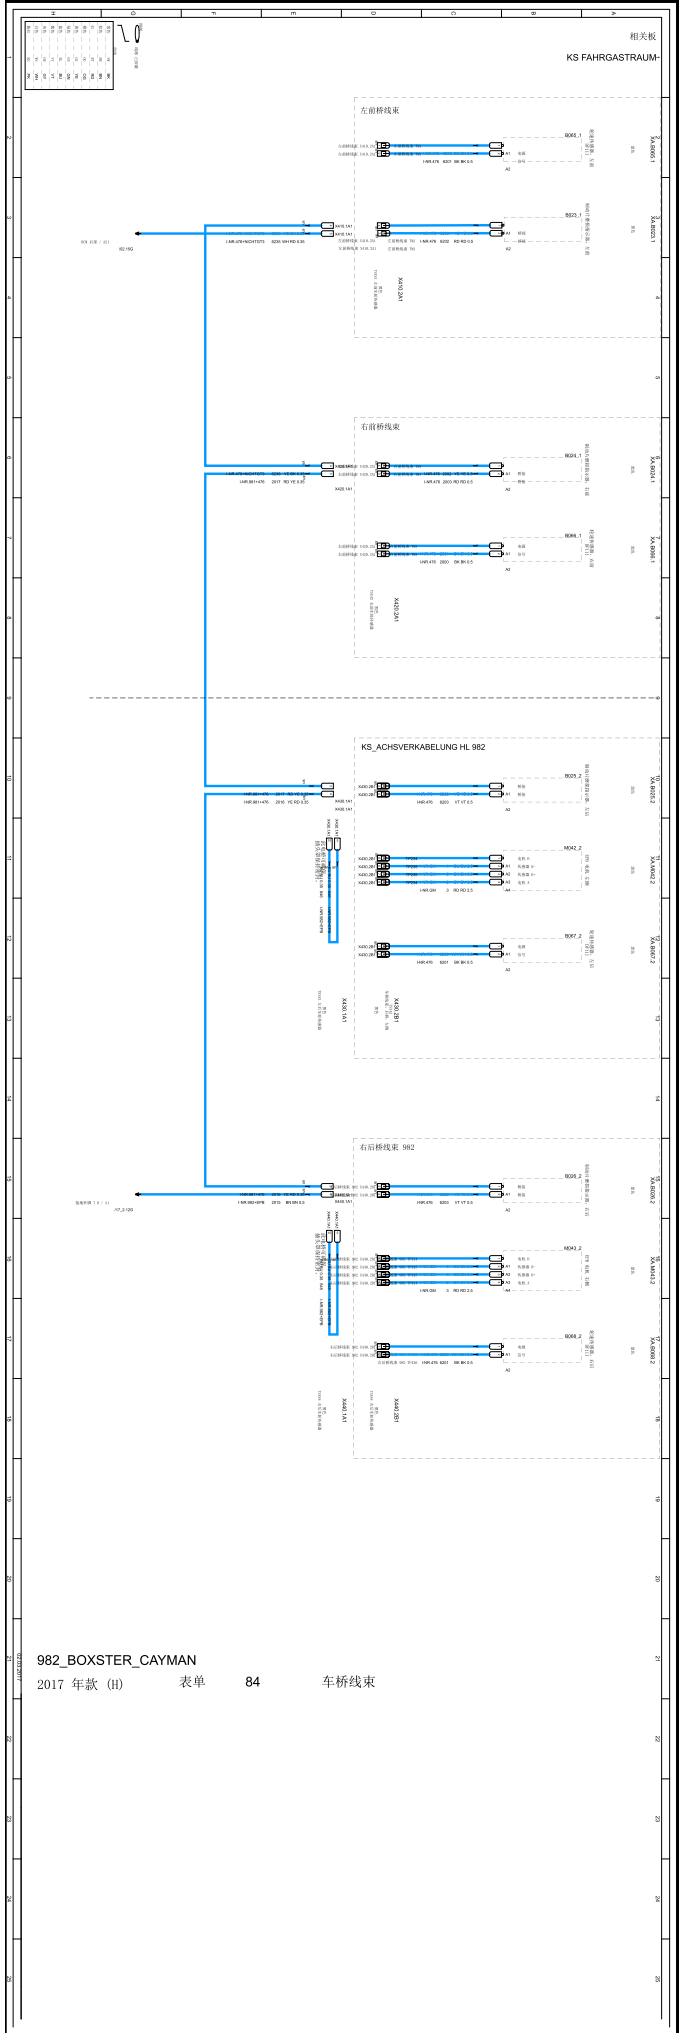

(84) 车桥线束

显示/隐藏导航栏